



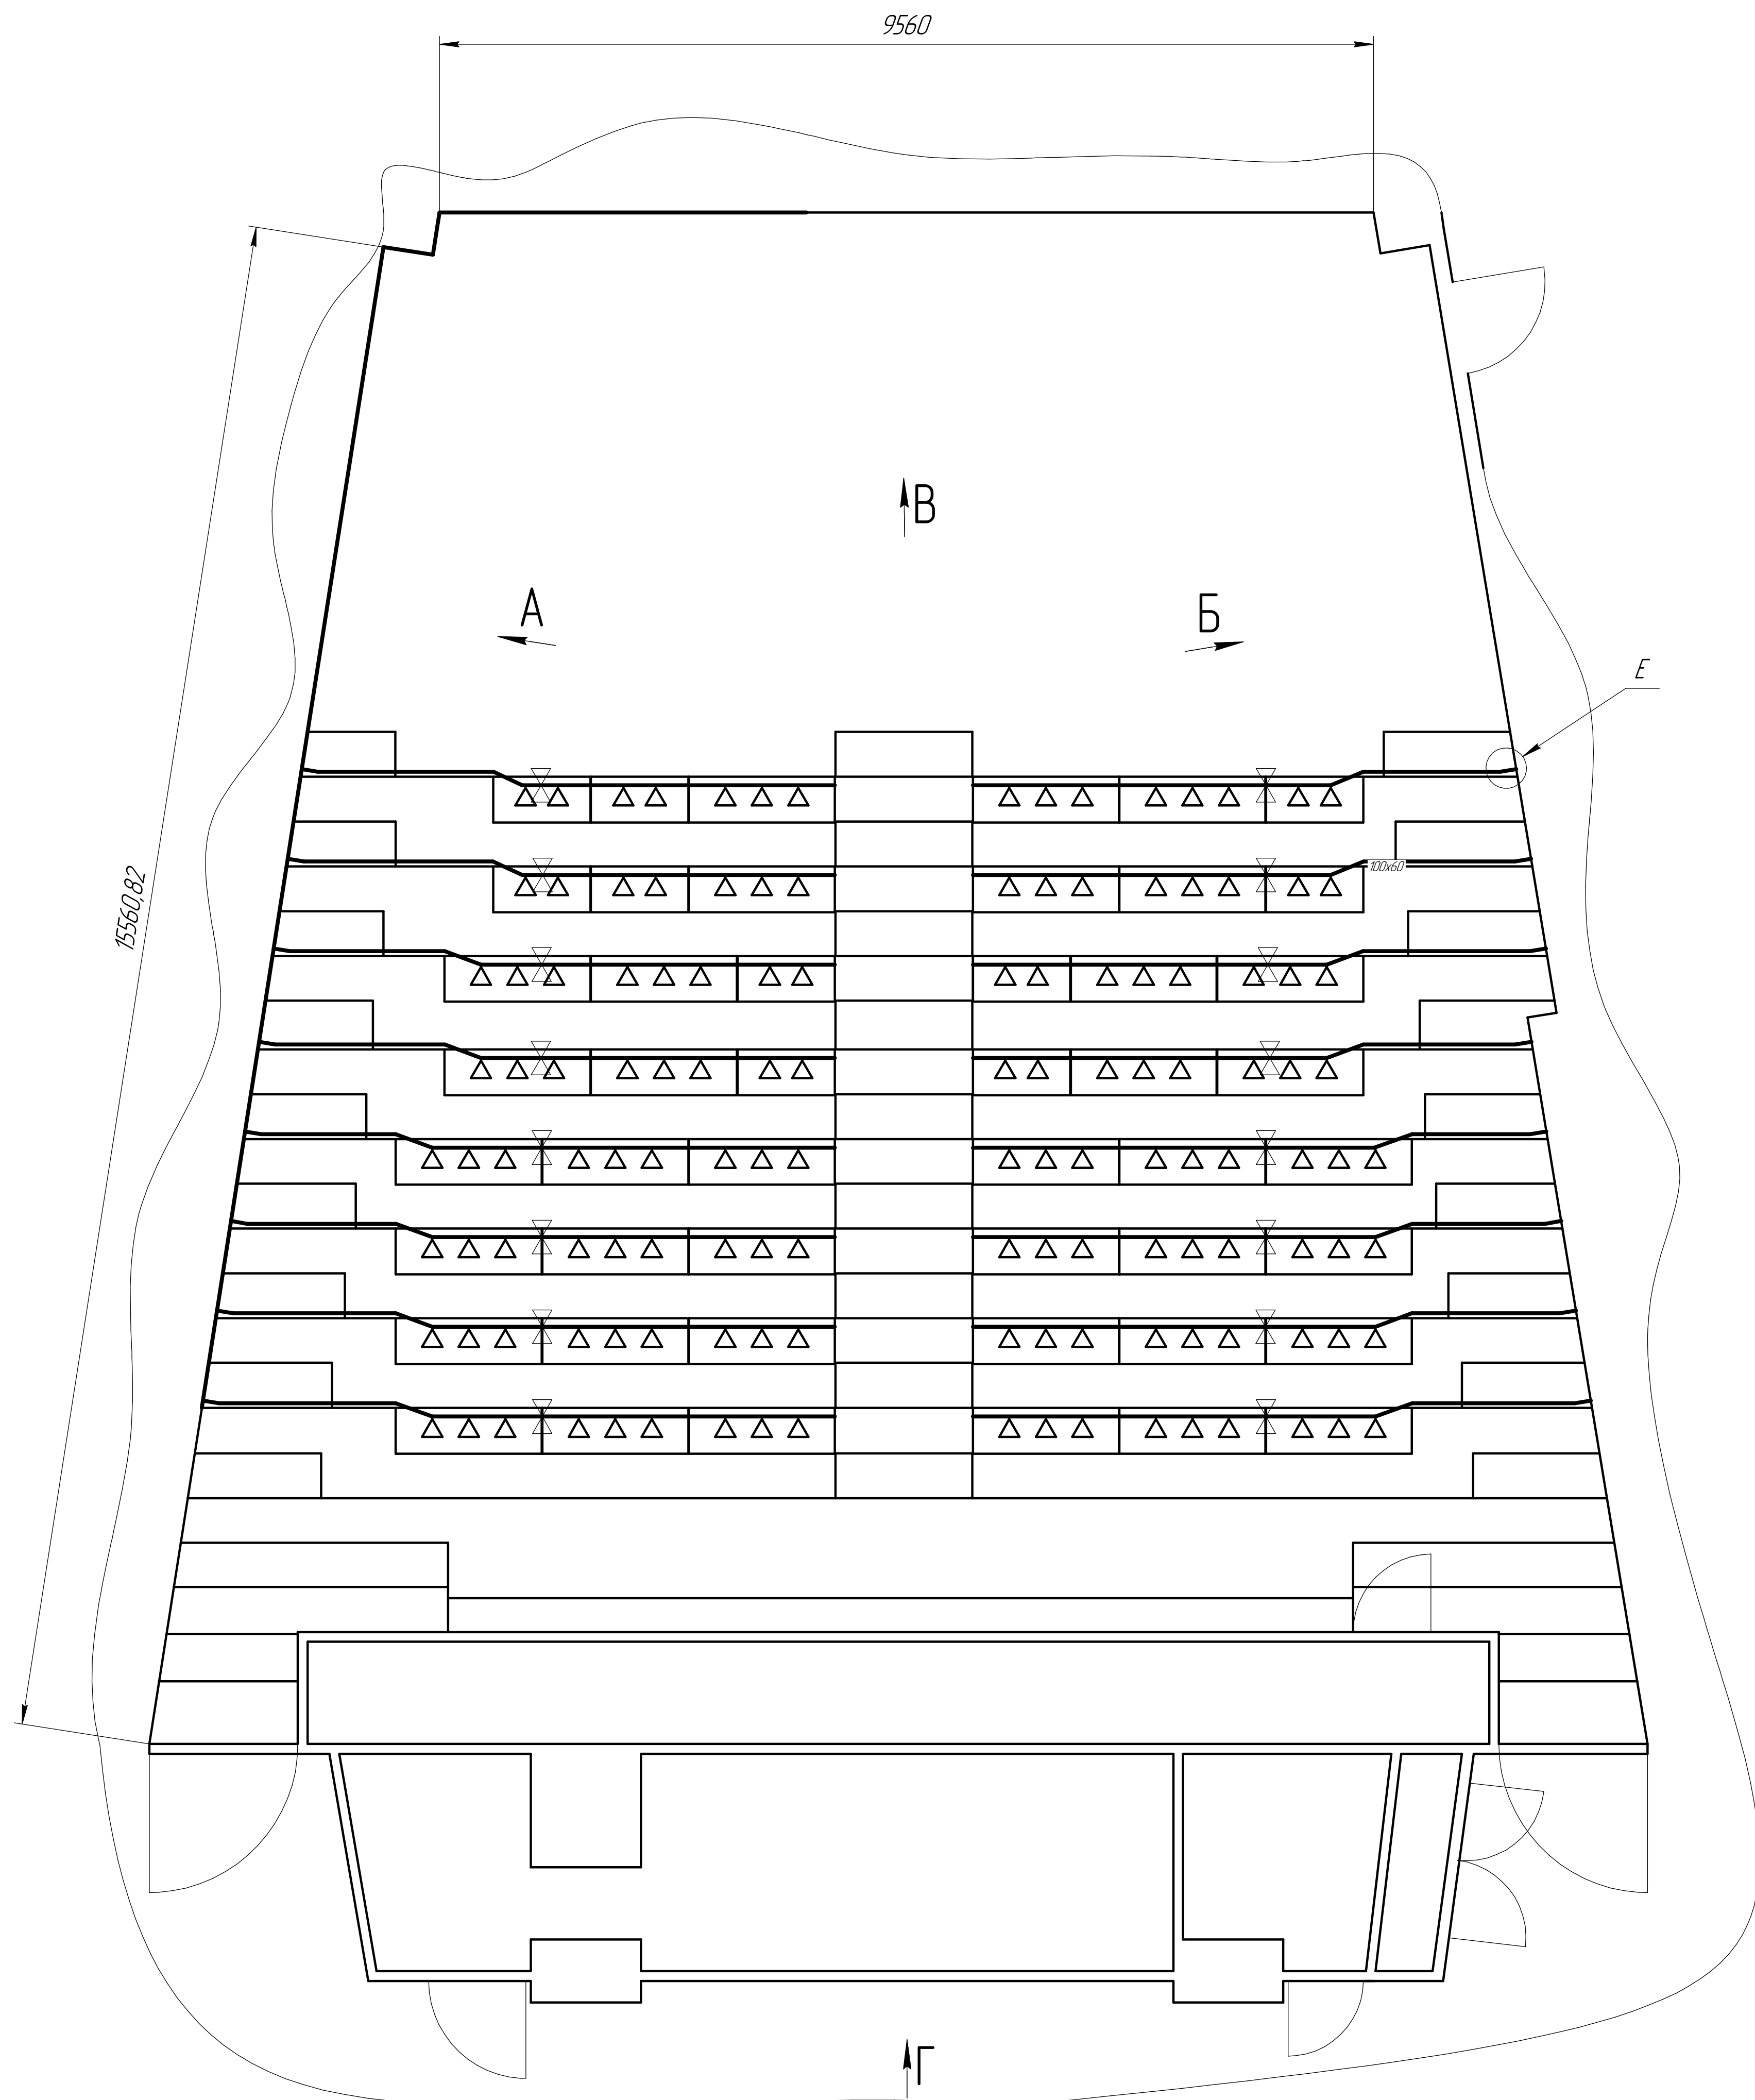


E (1:2)

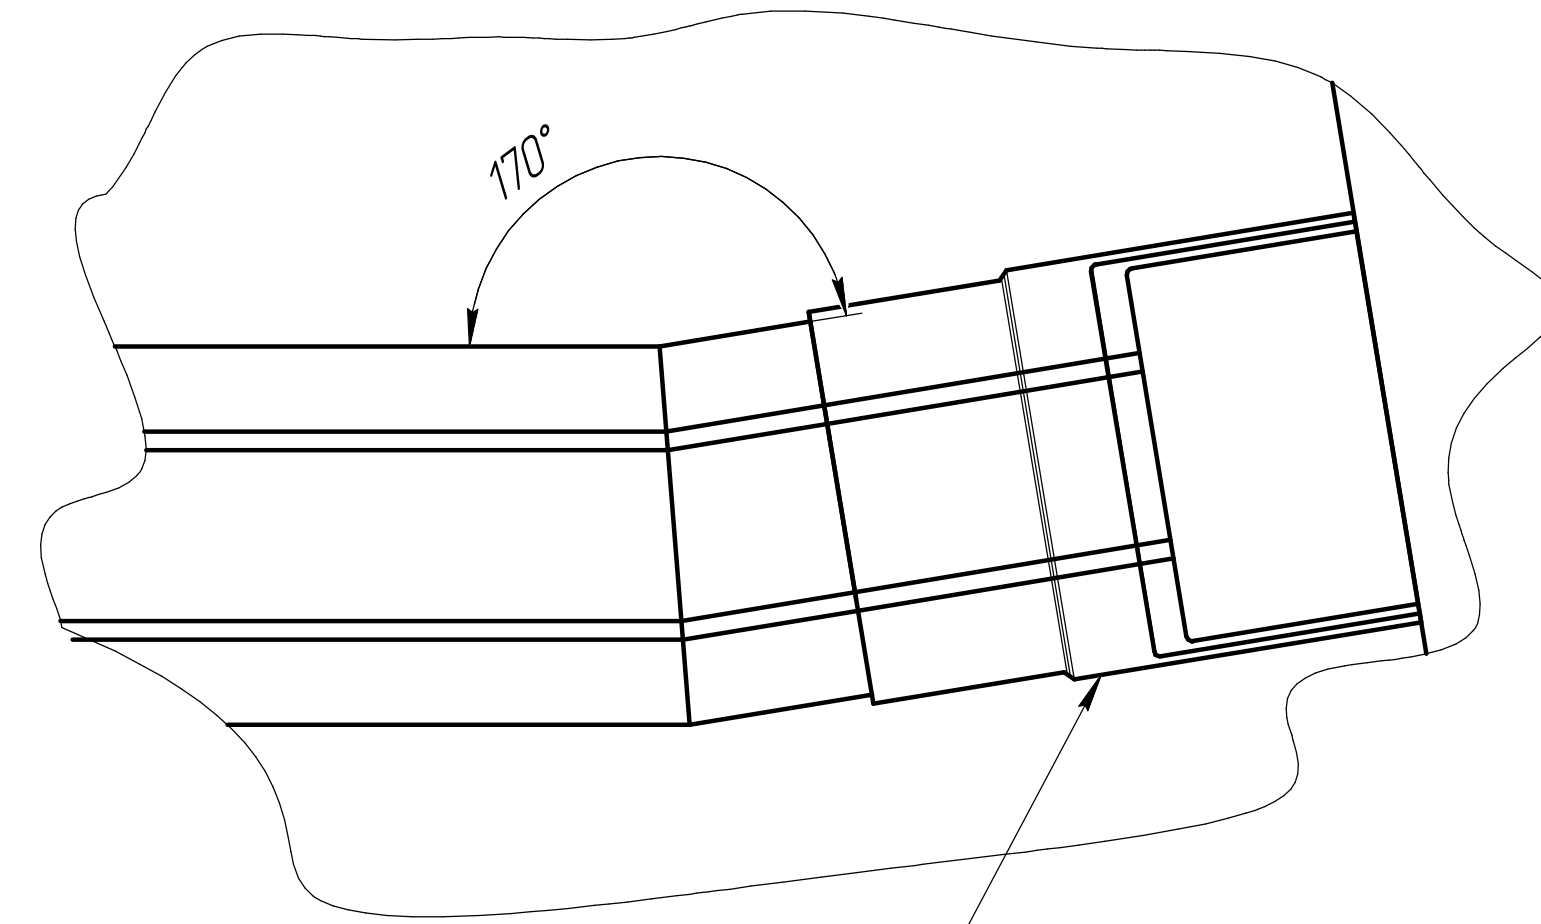

Угол внутренний изменяемый $NIAV$

Кабель под рабочим столом

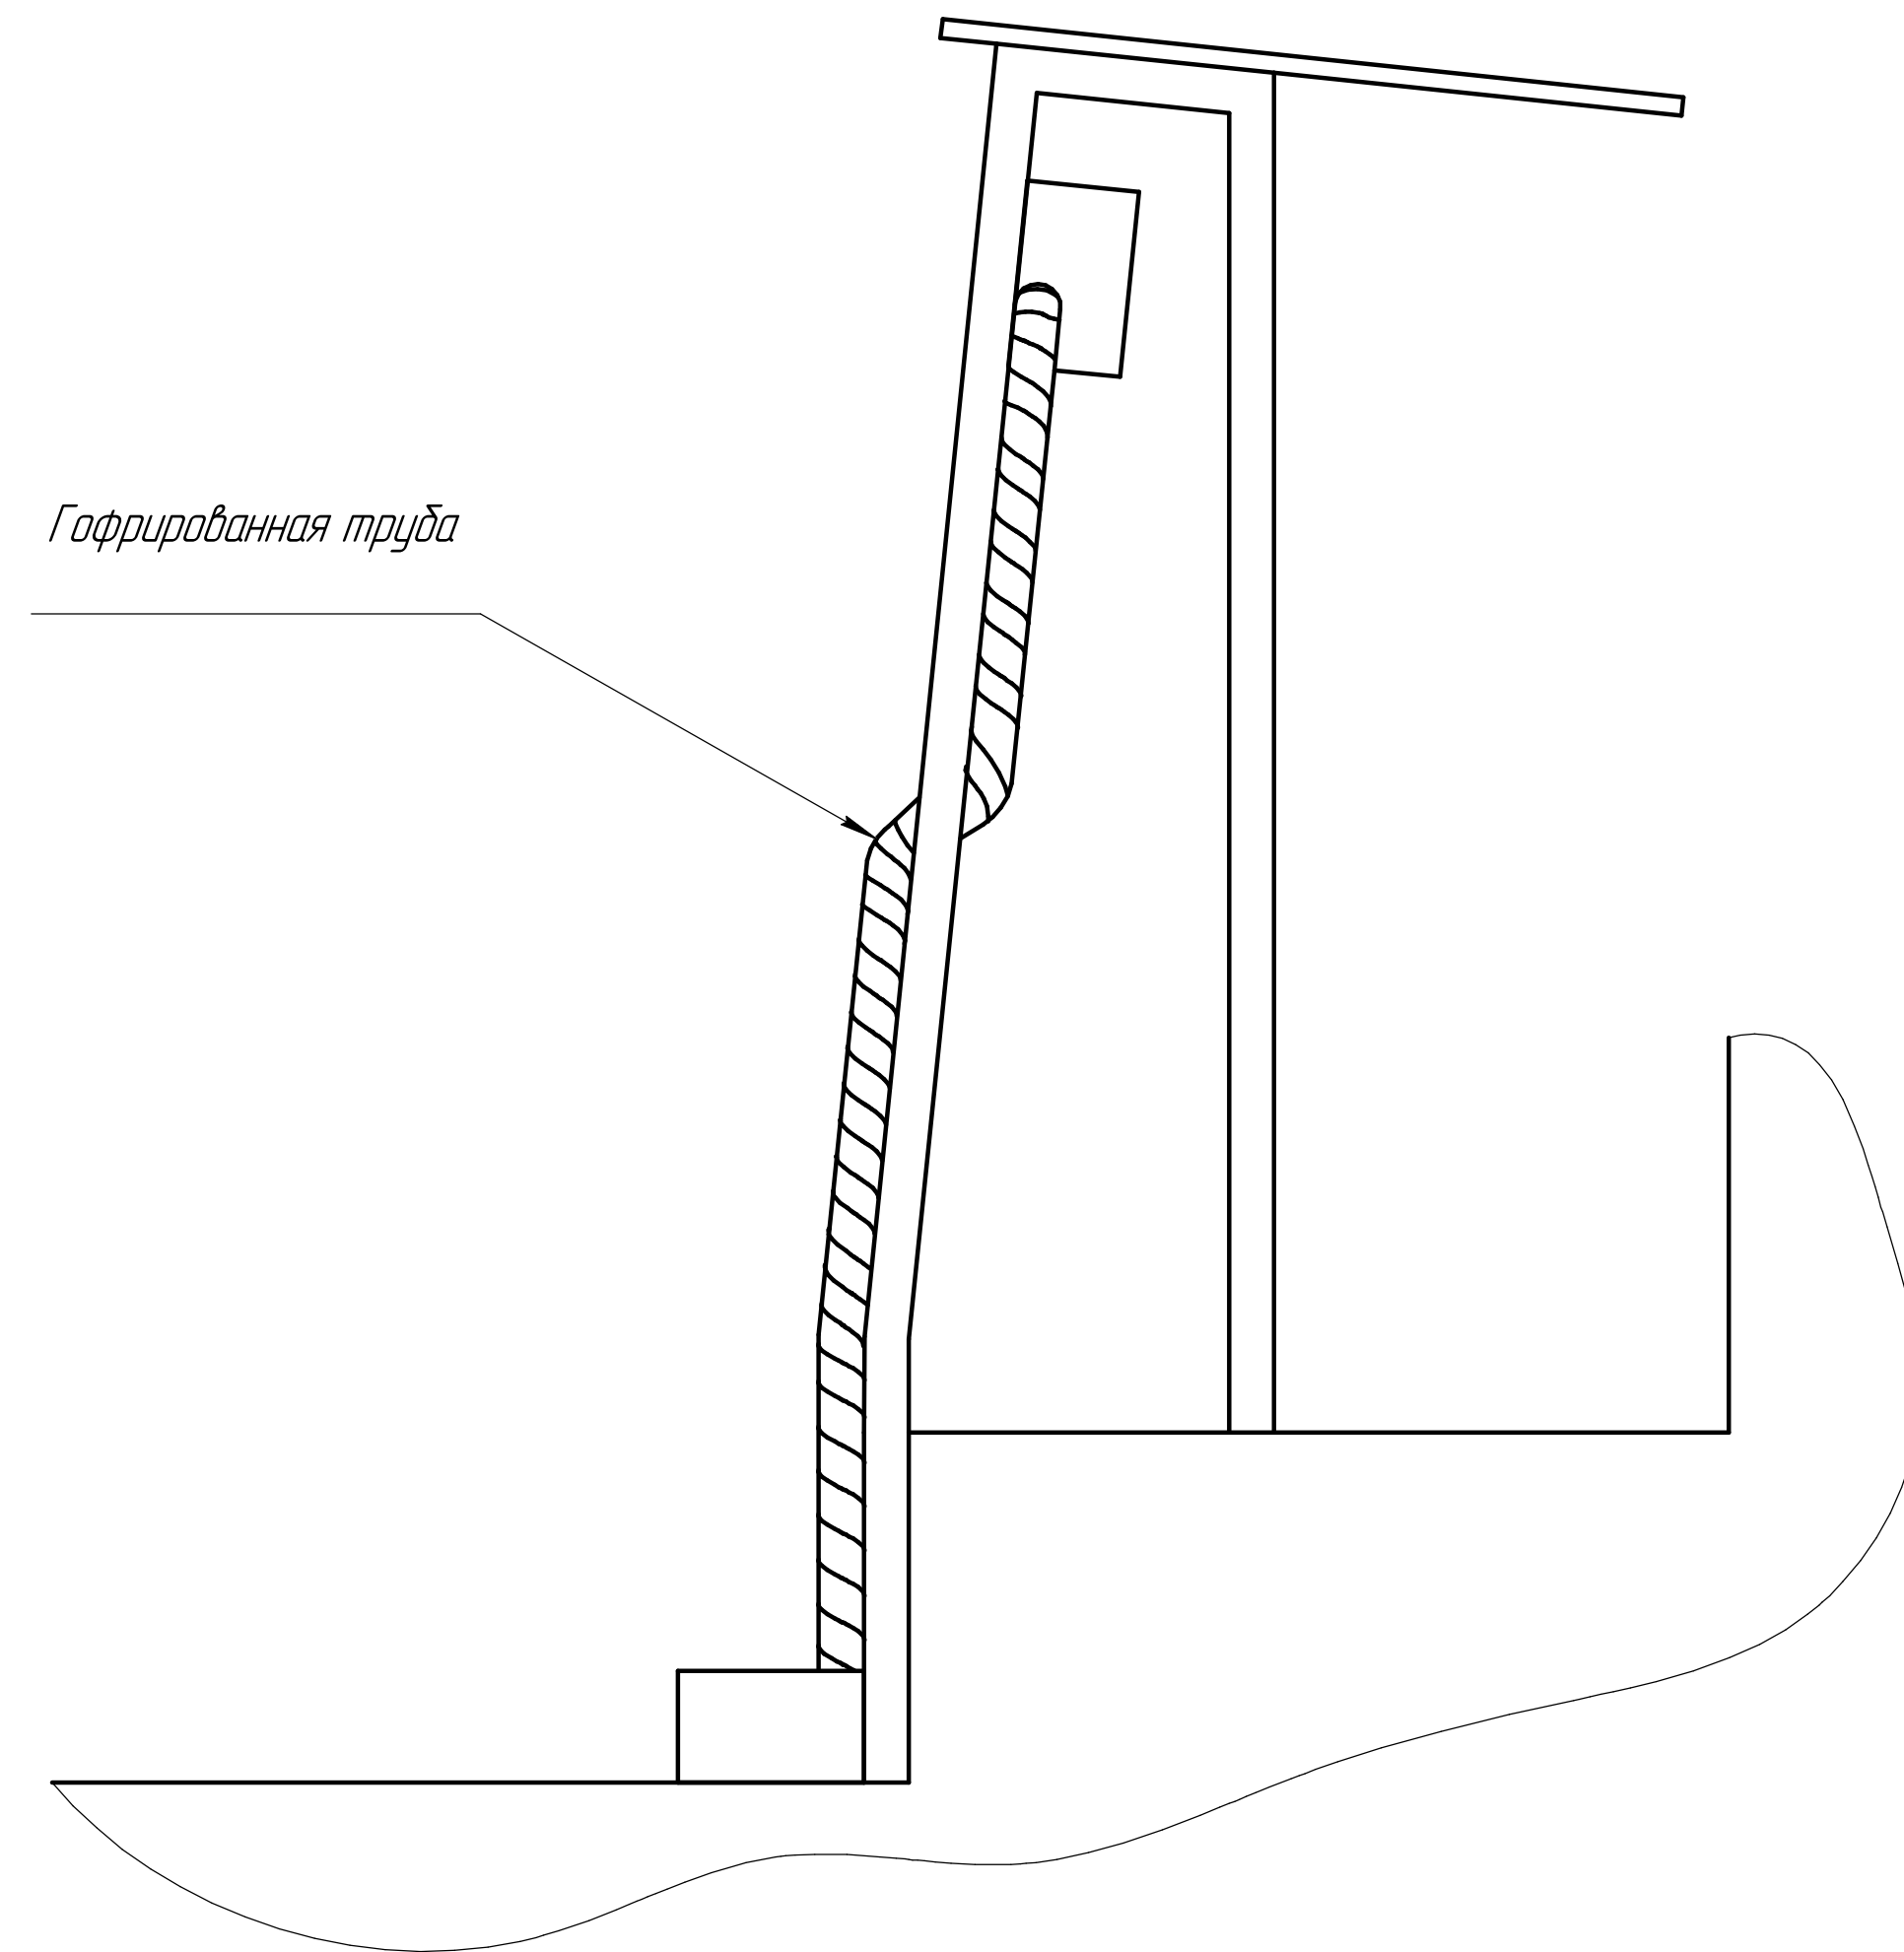

Гофрированная труба

 *соединение лотков*

[illegible]

КОМПАС-3D v23 Учебная версия © 2024 ООО "АСКОН-Системы проектирования", Россия. Все права защищены.
Инд. № подл. Подп. и дата
Инд. № подл. Подп. и дата
Инд. № подл. Подп. и дата

Не для коммерческого использования

МГТУ.24.4536.СС

A (1:1)

Ж (1:10)

E (1:4)

Тройник-отвод NTAN

Кабель-канал 120x80

Кабель-канал 100x60

Фальшь-ступень

На всю протяженность стены вдоль лестницы
установлены кабель-каналы

Изм.	Лист	№ докум.	Подп.	Дата

МГТУ.24.4536.СС


Копировал

Формат А2

Лист
2

МГТУ.24.У536.СС

Б (1:1)

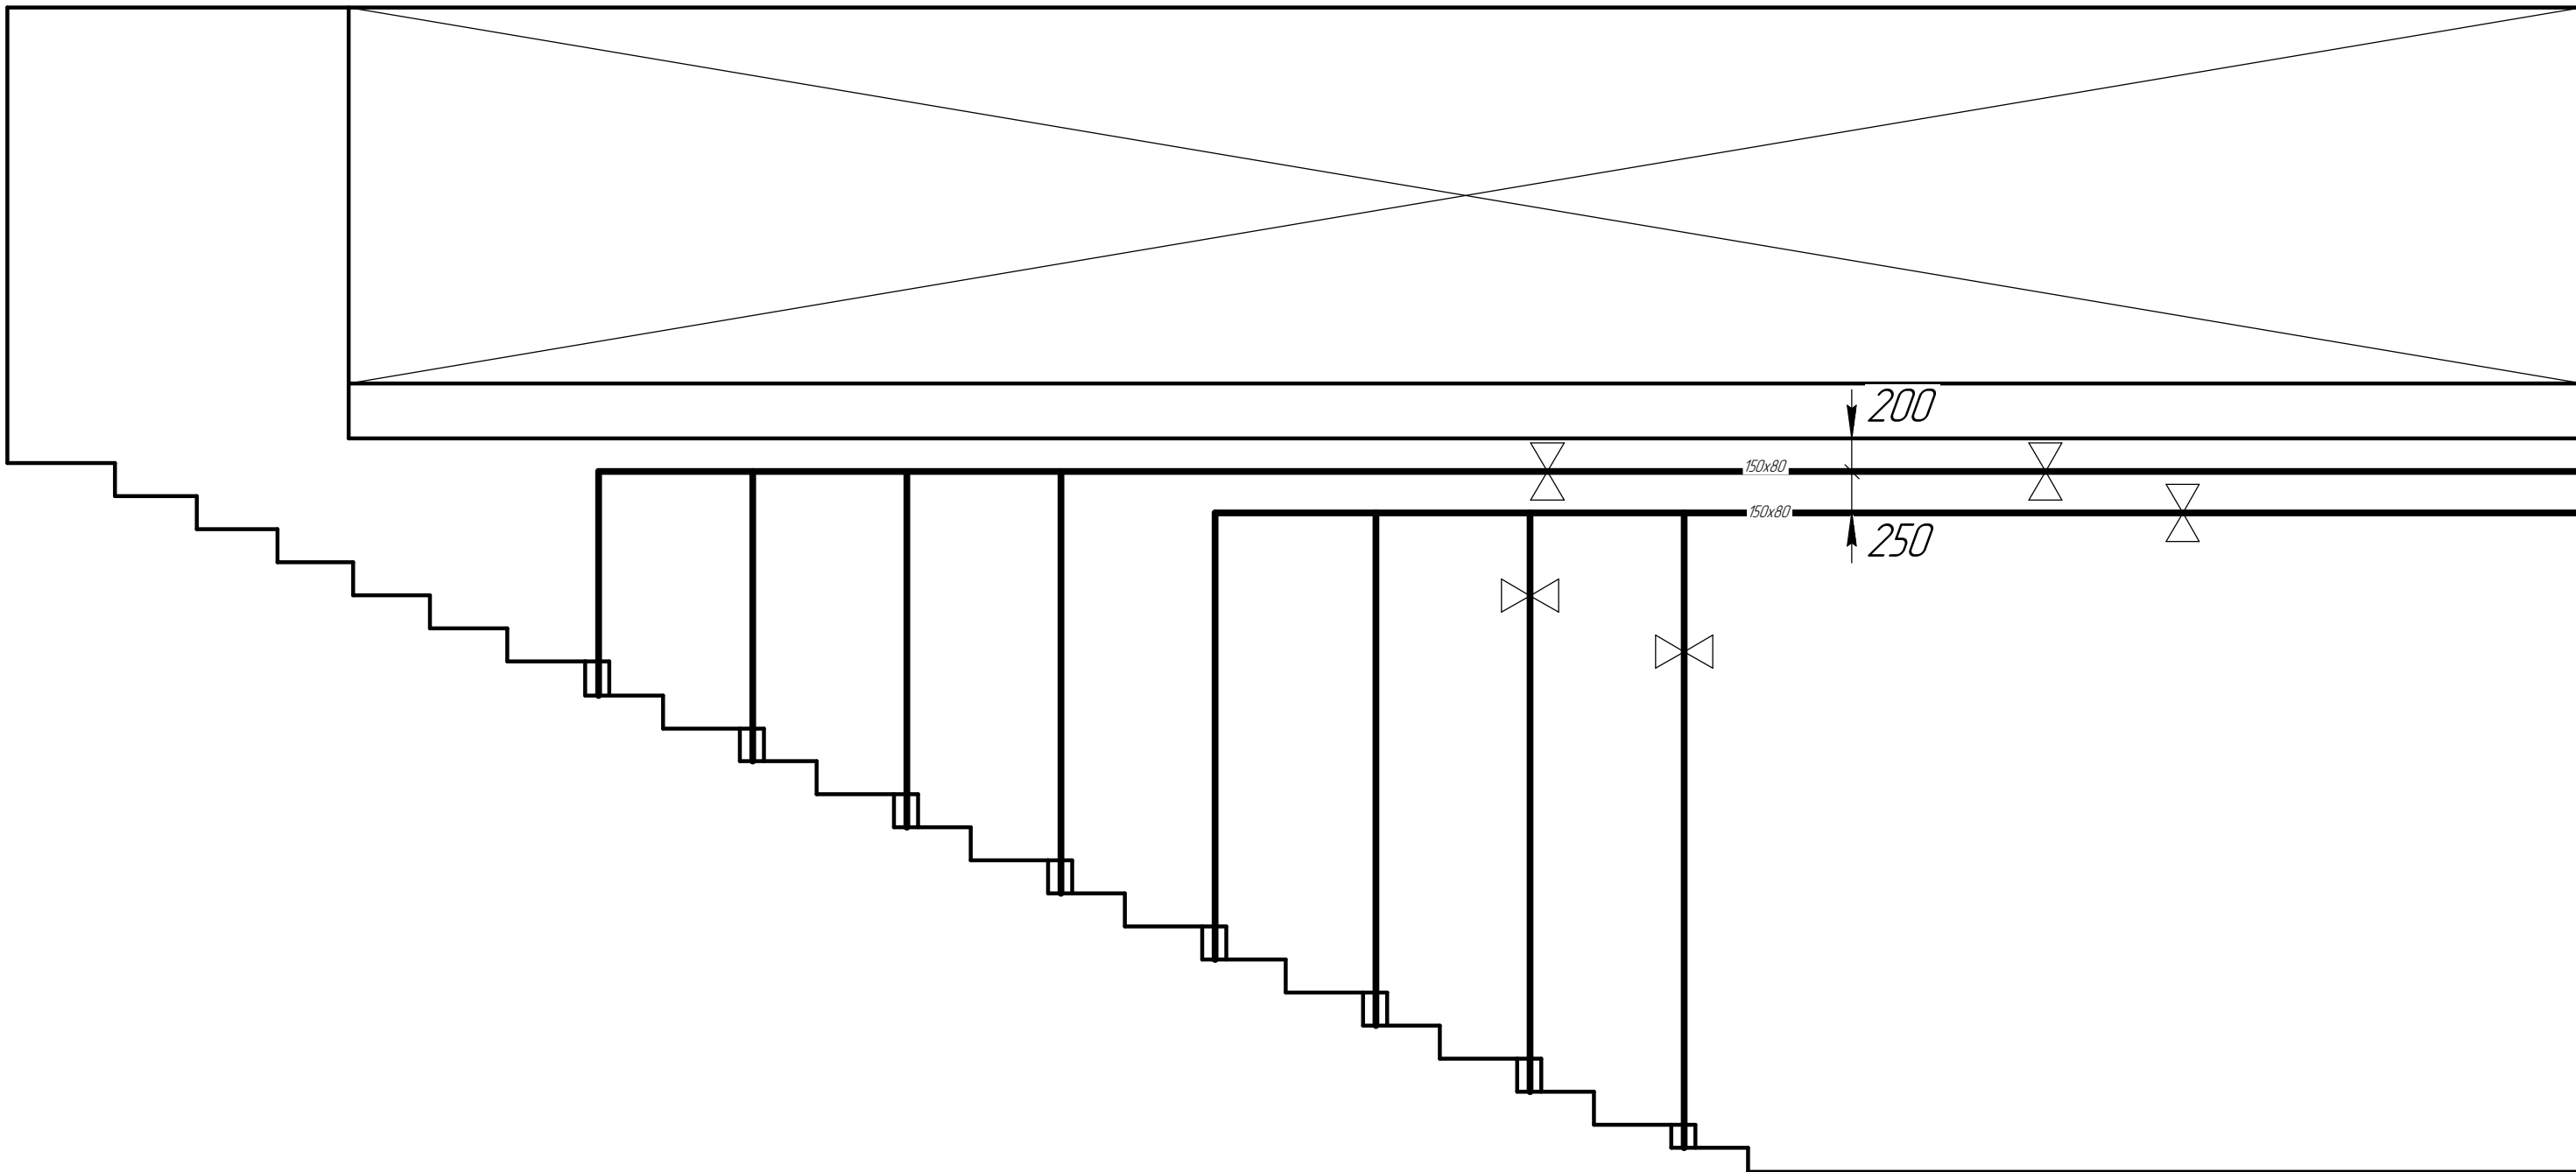

Изм.	Лист	№ докум.	Подп.	Дата

МГТУ.24.У536.СС

Лист
3

В (1:1)

Переход от кабель-канала к лотку посредством угла внешнего изменяемого NIAV

70

Фальш-потолок

3520

250


150x80

150x80

И

Д-Д


МГТУ.24.4536.СС

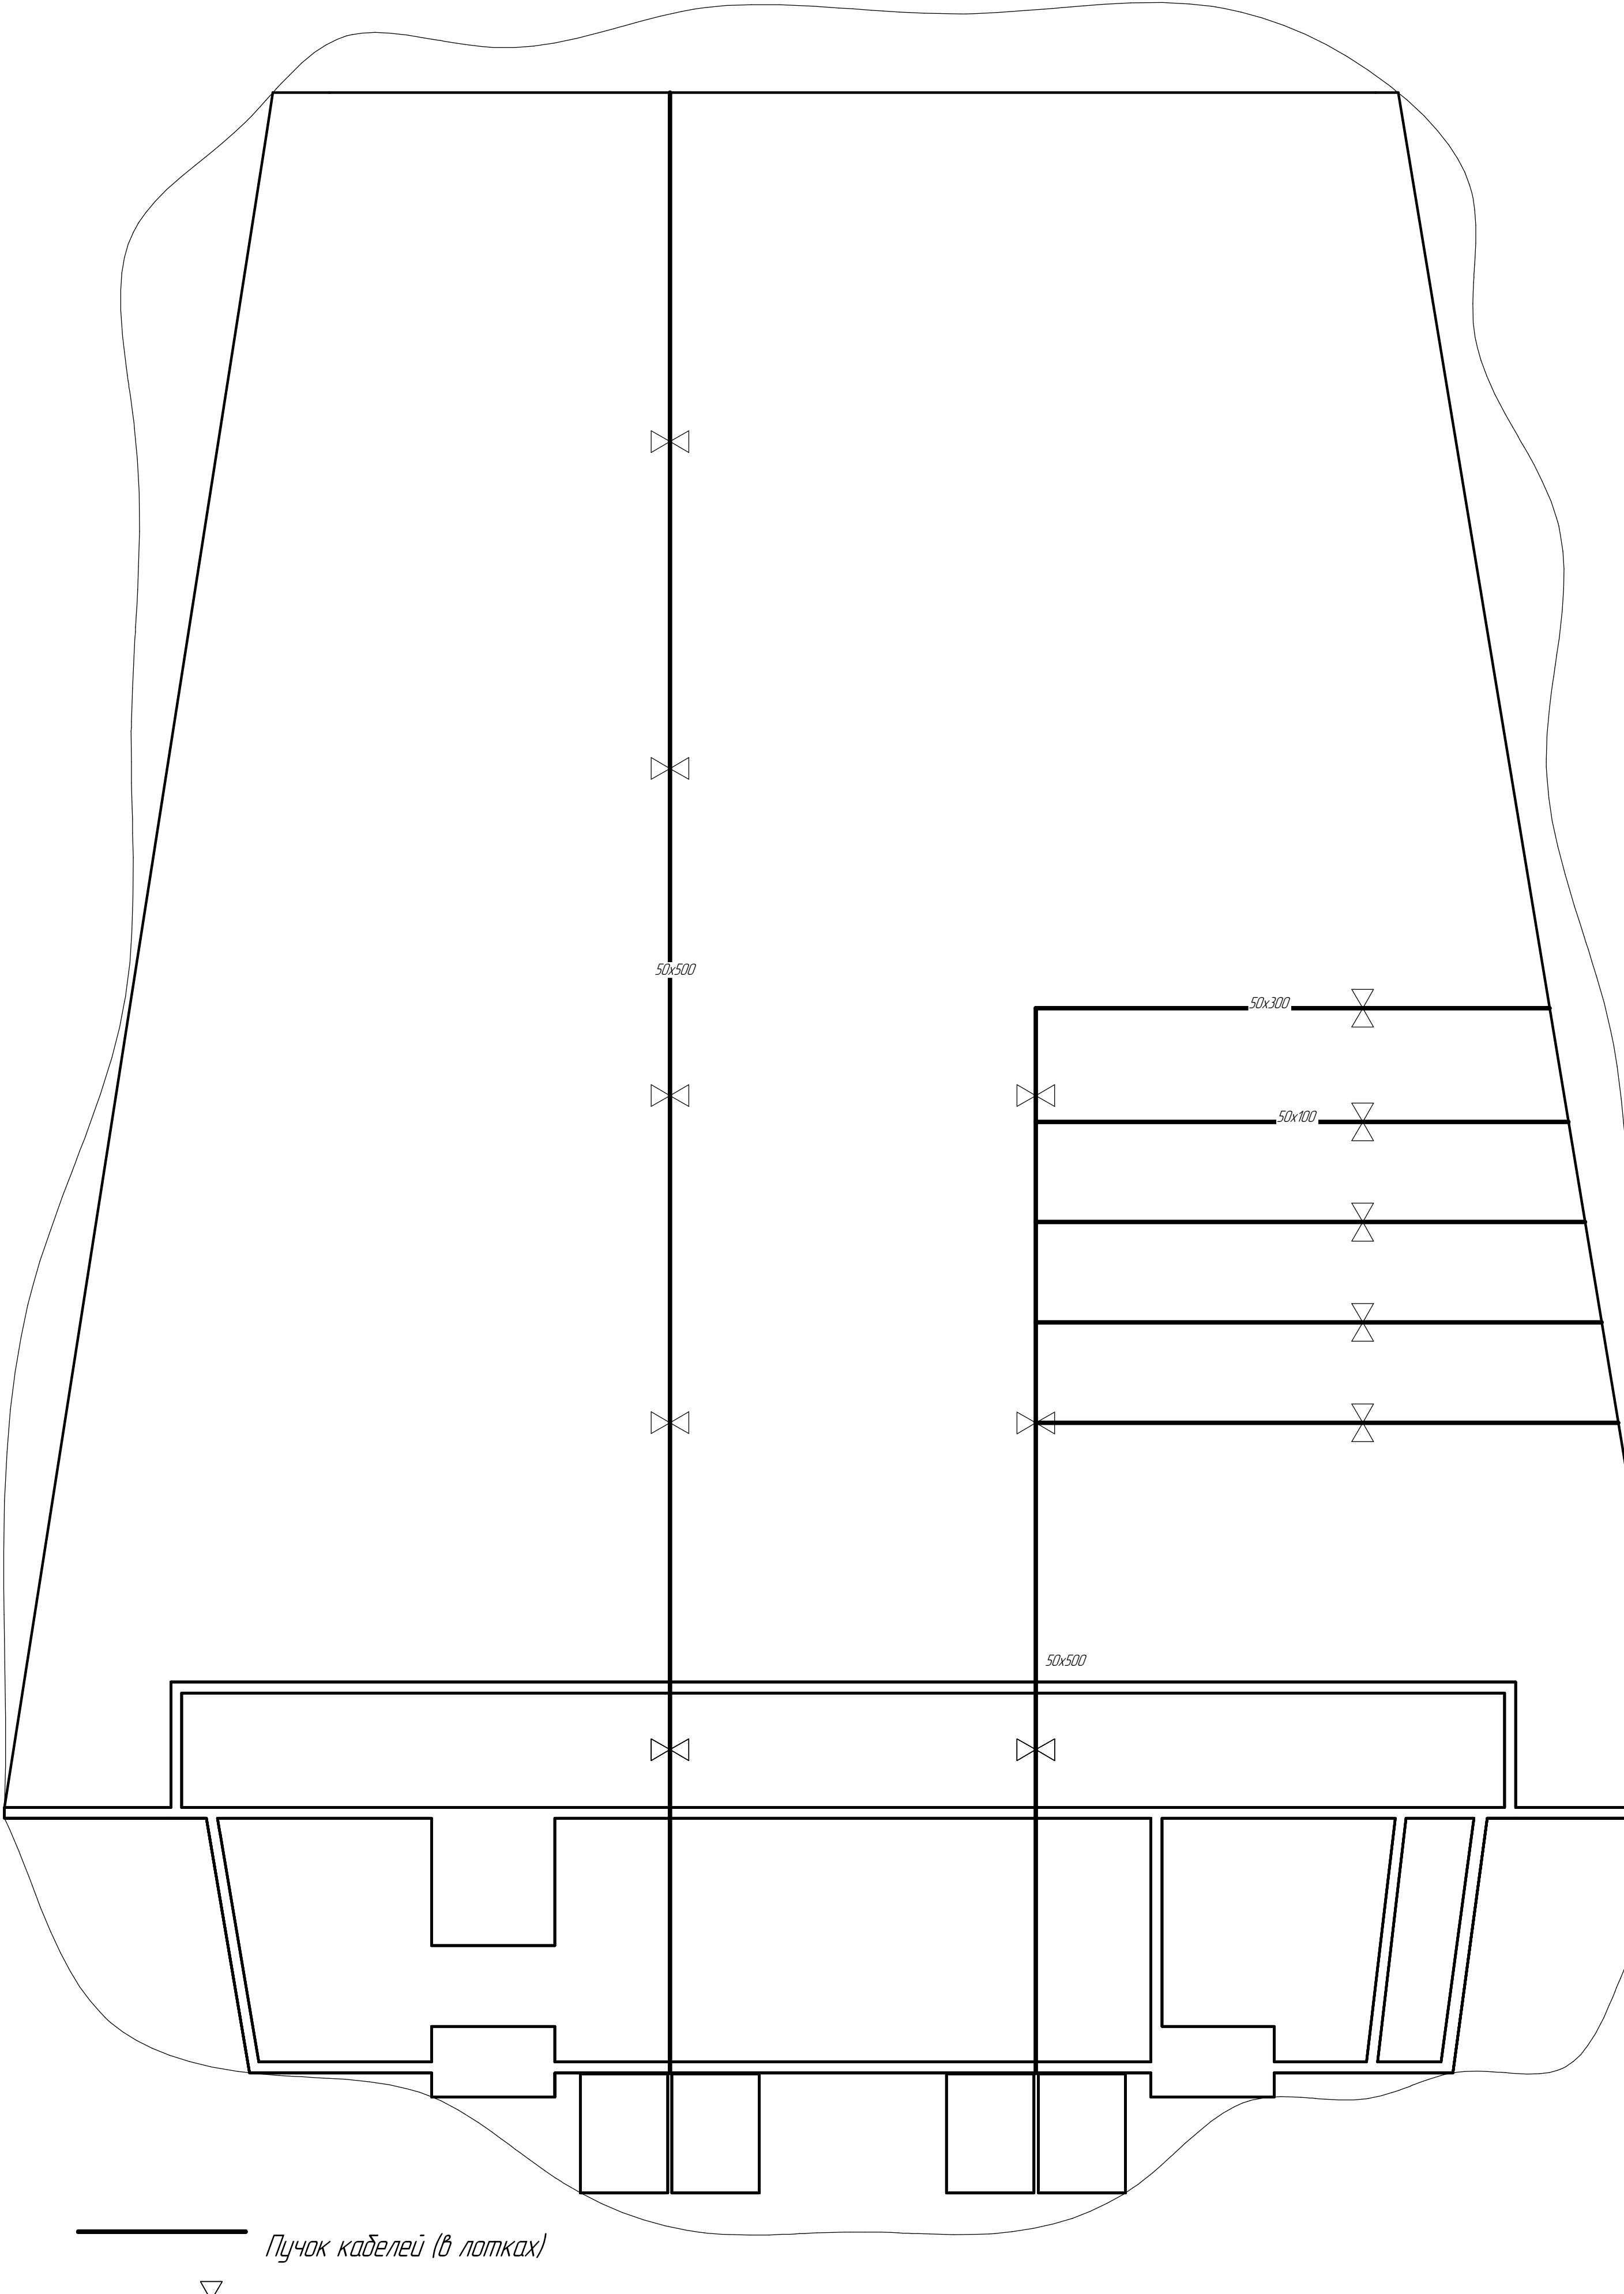


— Пучок кабелей (в лотках)
X Соединение лотков

						МГТУ.24.4536.СС	Лист
Изм.	Лист	№ докум.	Подп.	Дата			5


Копировал _____ Формат А2

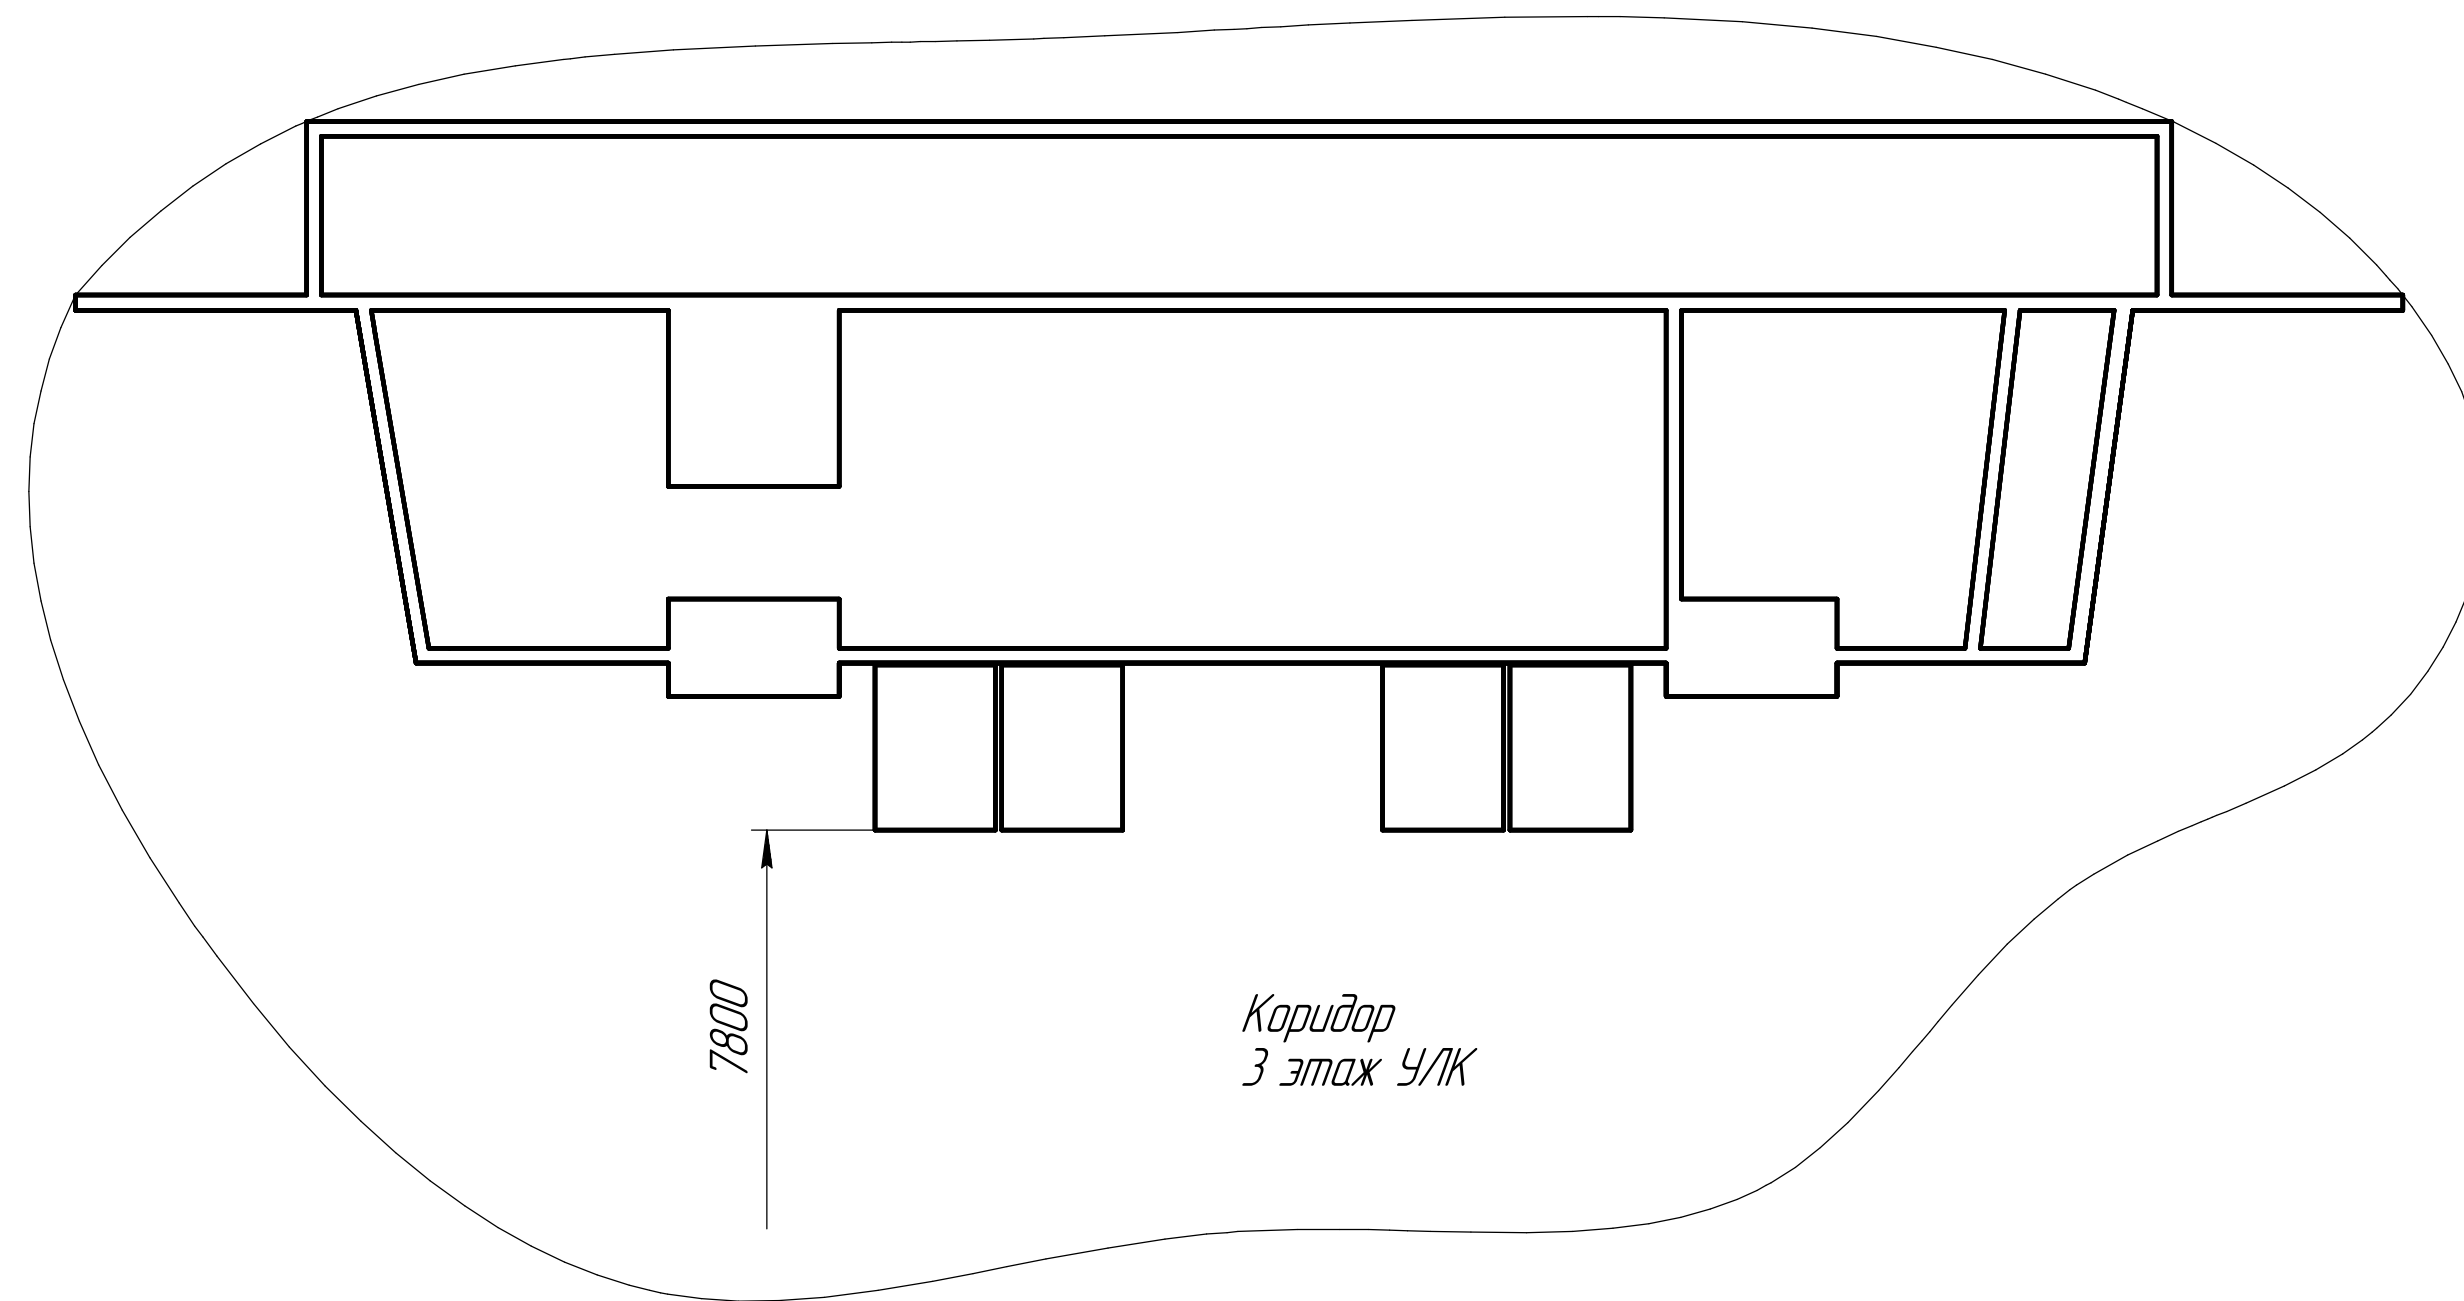


Г (1:10)

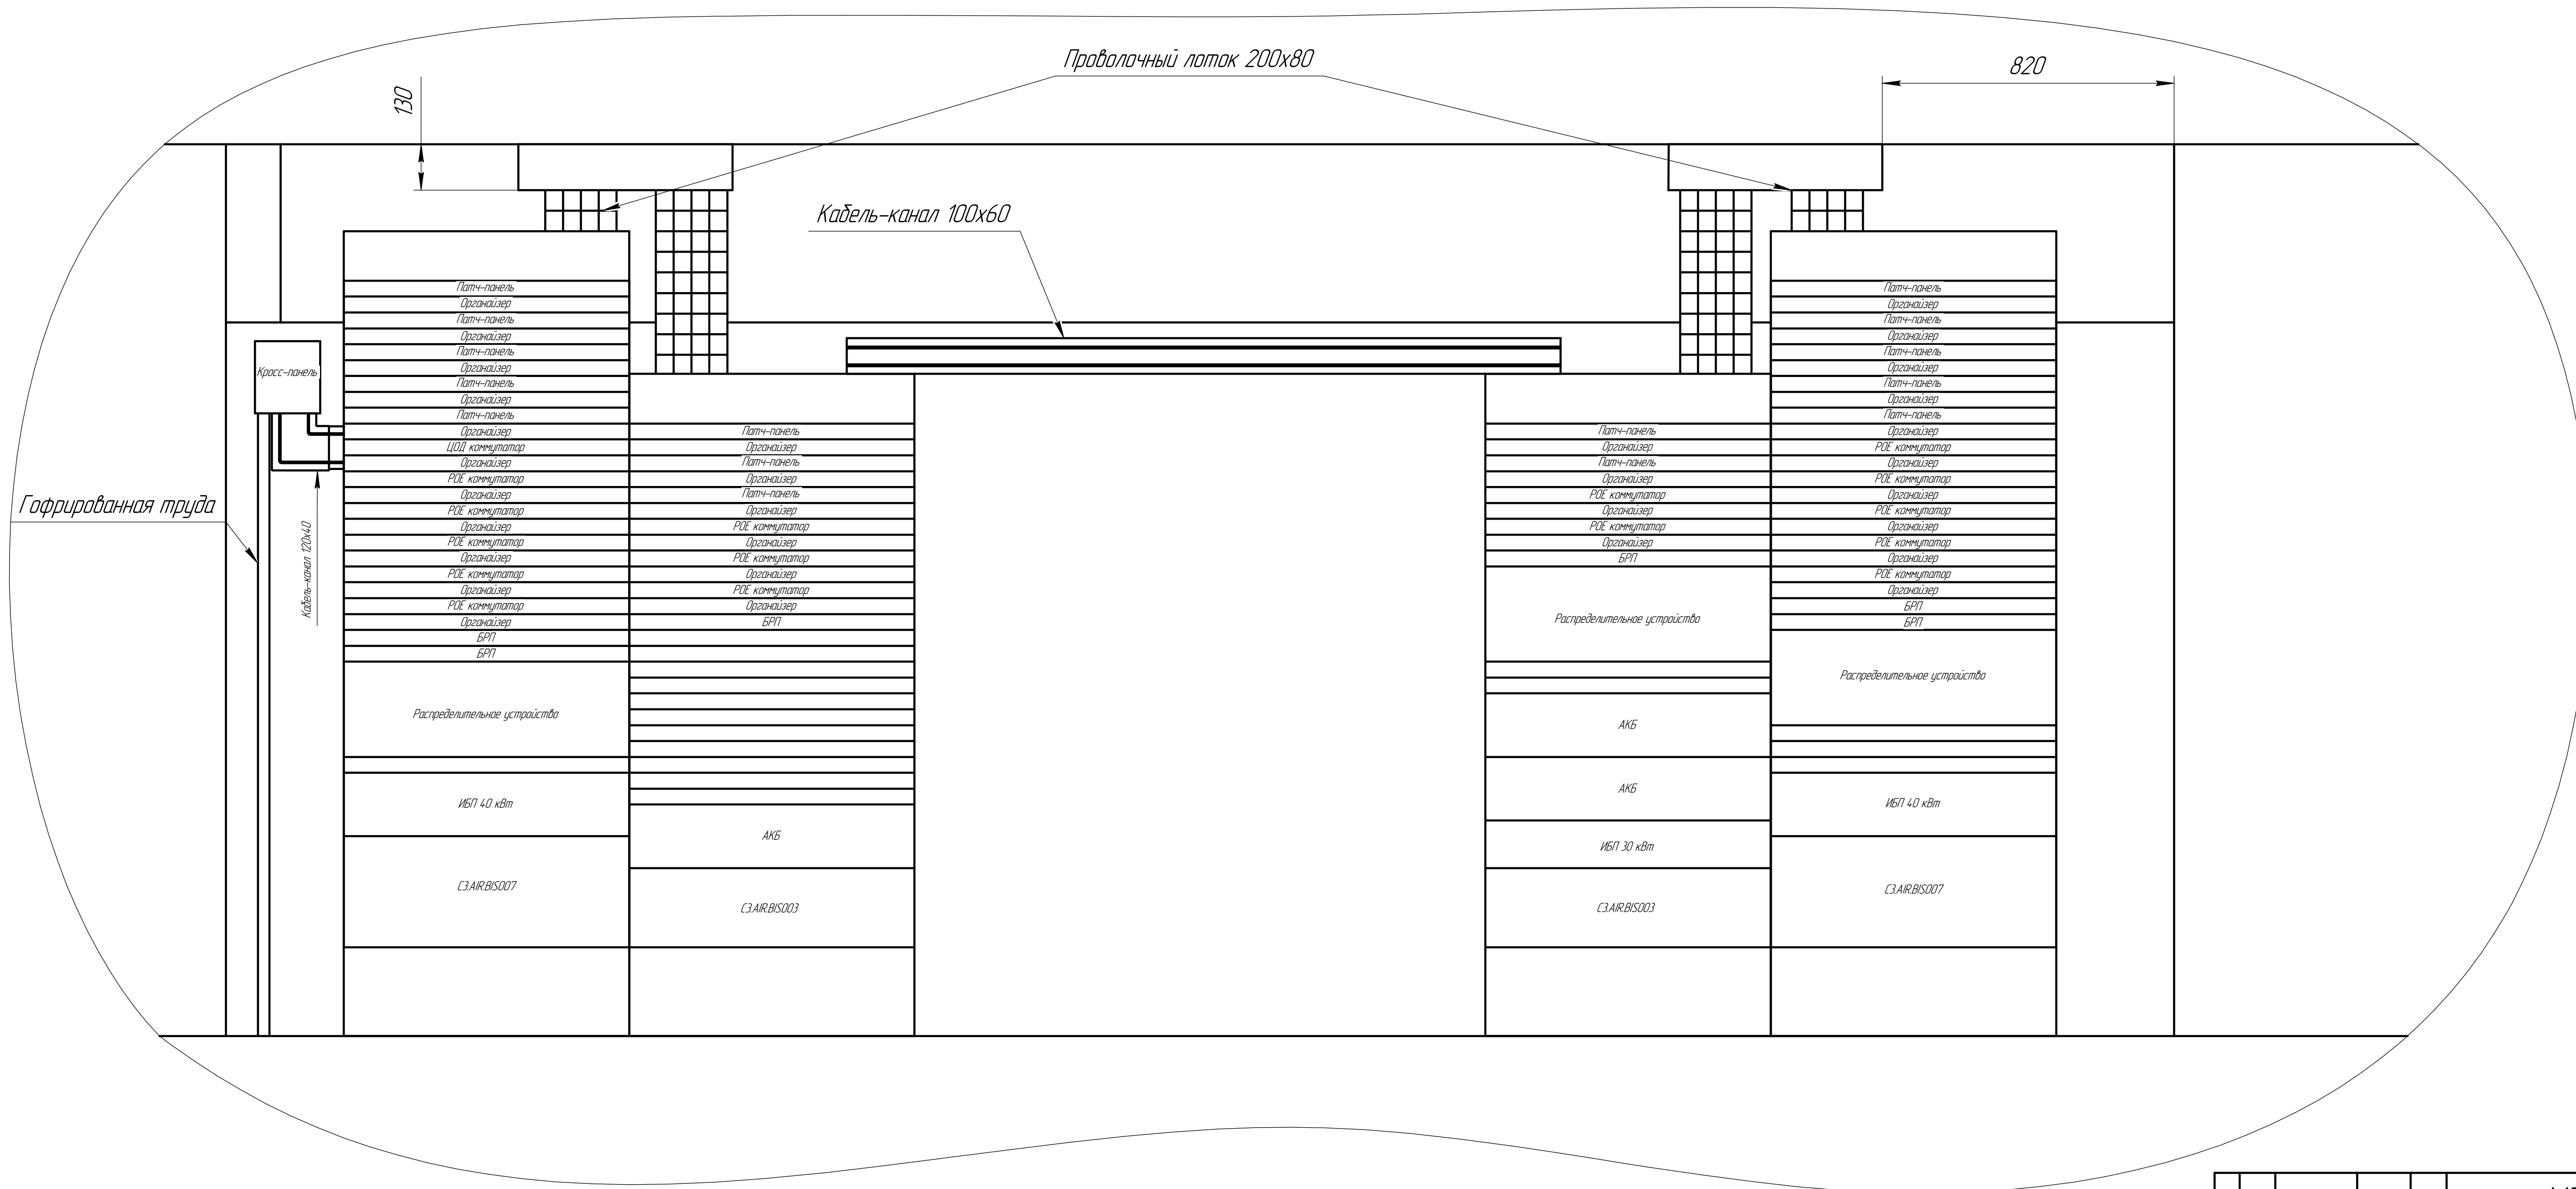


И (1:10)

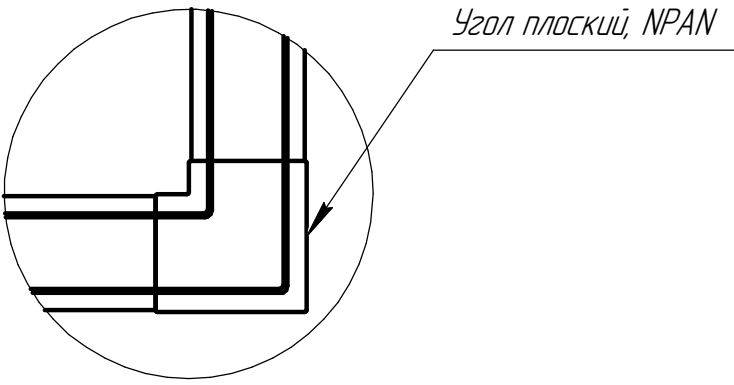

К (1:2)

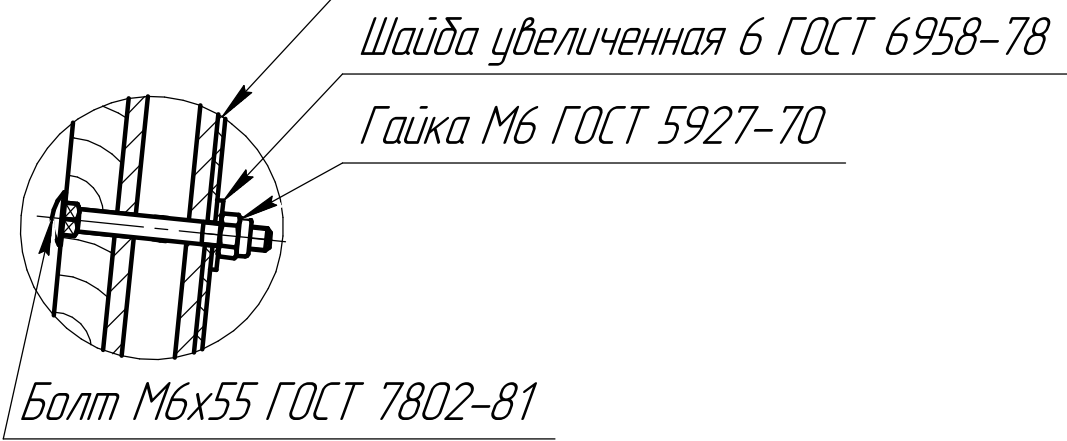

Крепление кабель-канала к медельному уголку

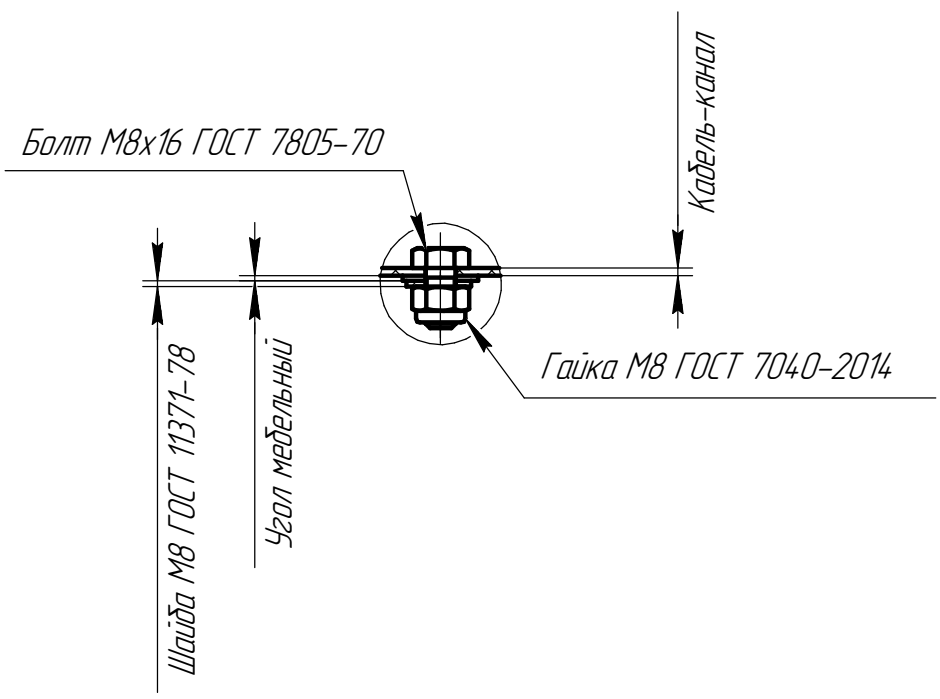

После кабель-канала кабеля идуи по гофре, которая выходит из парты и заходит в кабель-канал, который крепится на медельные уголки, а затем заходит в фальшь-ступень. Медельный уголок крепится анкерным болтом с гайкой.

Крепление кабель-канала к парте




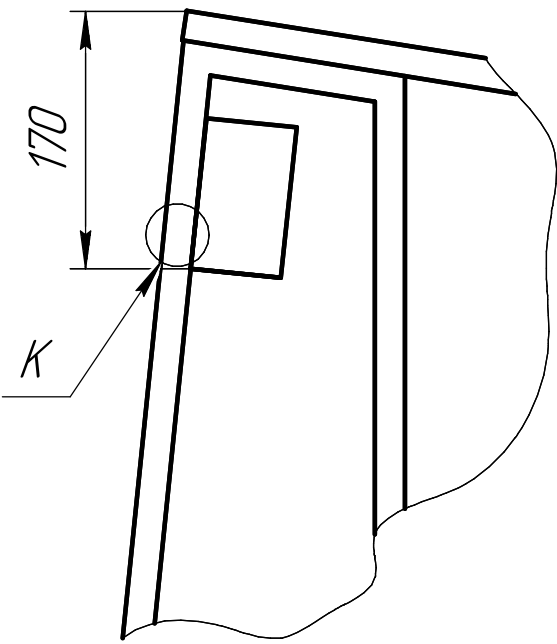


Схема крепления короба к лотку

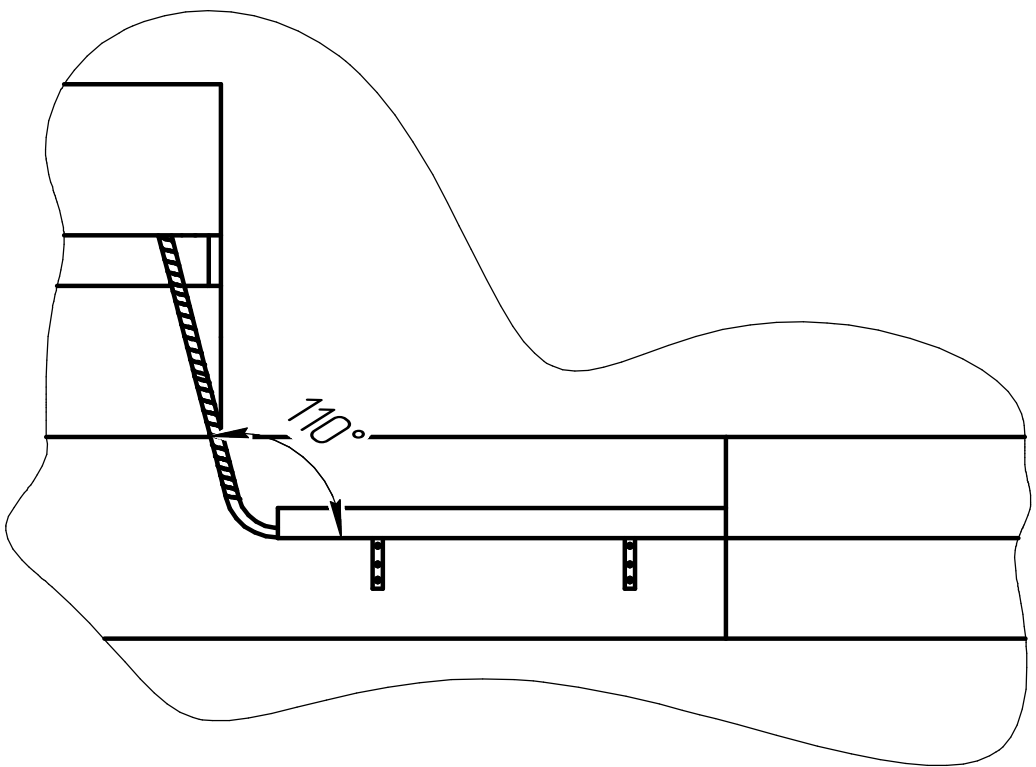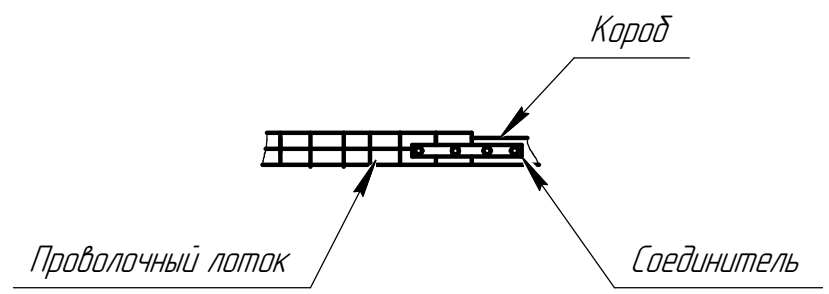

Расположение рамок-суппорт на кабель-канале

Рамка-суппорт на 6 модулей, PDA-3DN

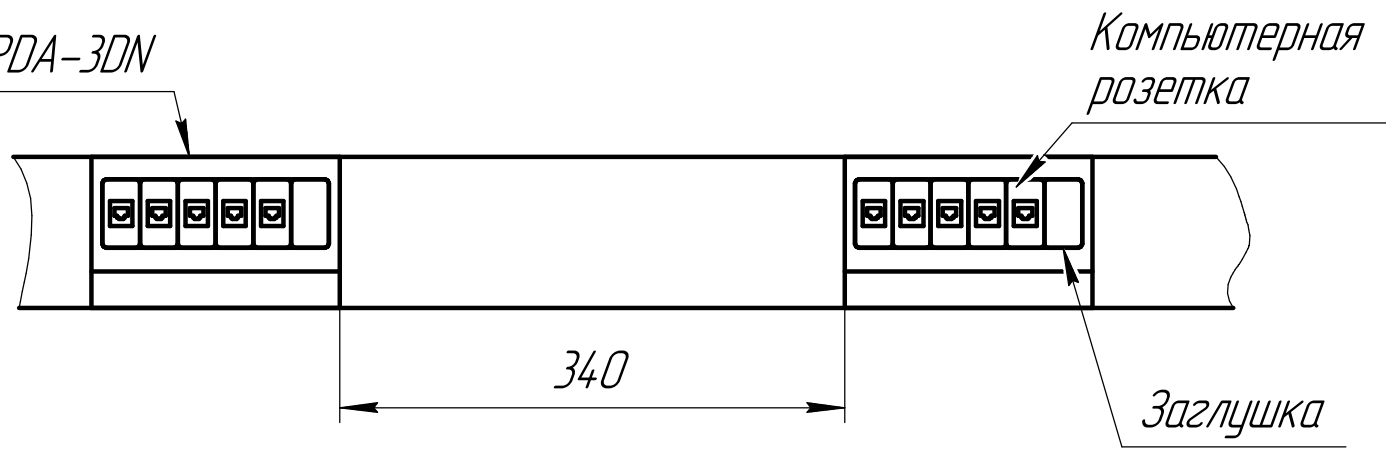

КОМПАС-3D v23 Учебная версия © 2024 ООО "АСКОН-Системы проектирования", Россия Все права защищены

Инд. № подл.	Подп. и дата
Взам. инв. №	Инд. № дцкл.
Подп. и дата	Подп. и дата

Не для коммерческого использования


Изм.	Лист	№ докум.	Подп.	Дата

МГТУ.24У536.СС

Копировал


Формат А3

Крепление для лотков:



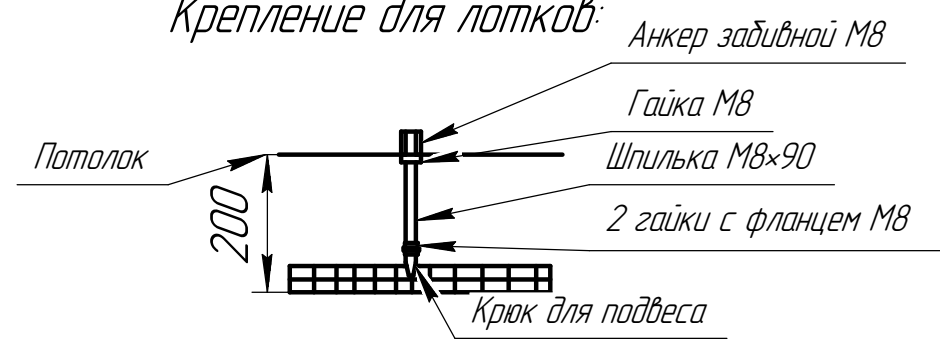


Поводок заземления крепится на стыках лотков при помощи соединительных комплектов



Крепление проволочного лотка осуществляется с помощью шпилек М8 у стен, у поворотов на 90°, а также каждые максимум 1,5 метра на участке до стены

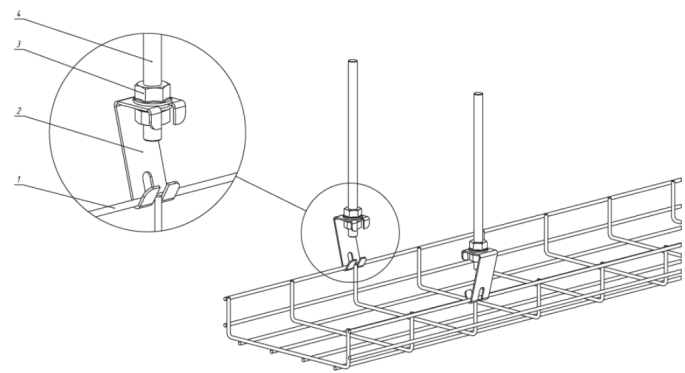

Соединения лотков

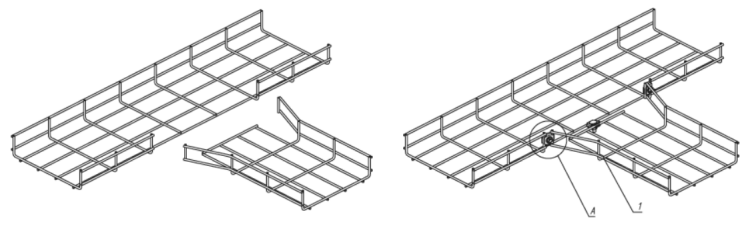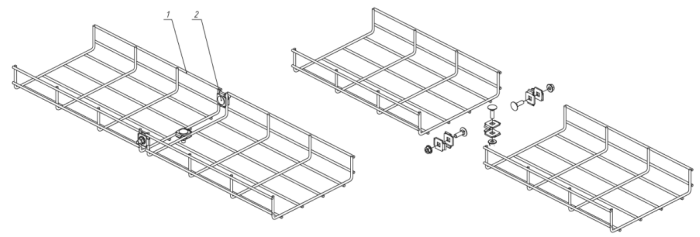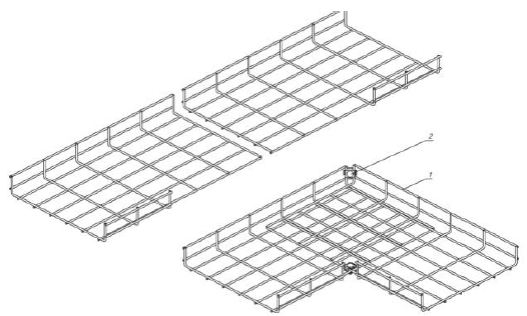

Проход лотка через стену

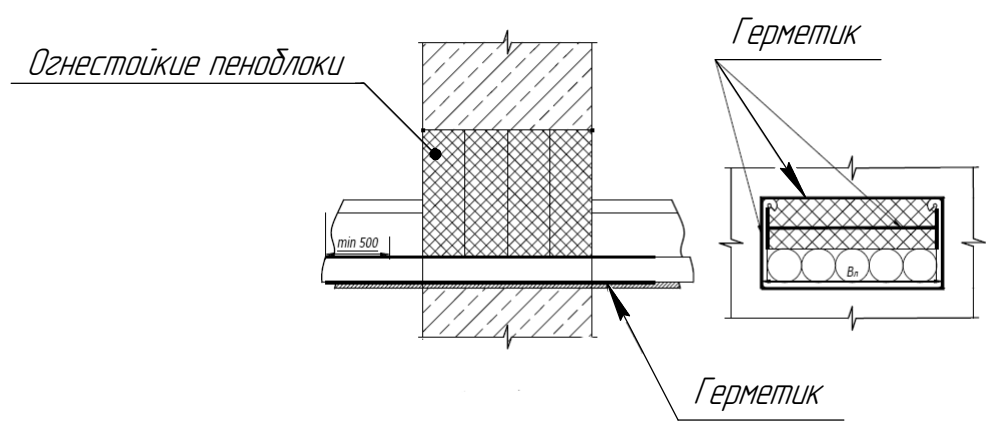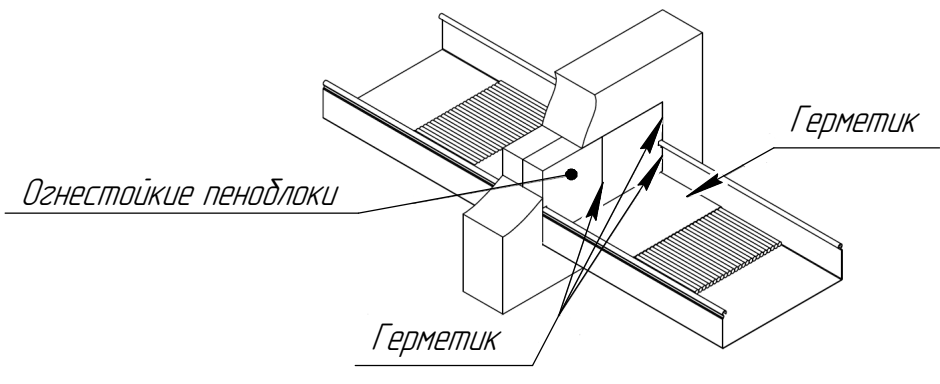

КОМПАС-3D v23 Учебная версия © 2024 ООО "АСКОН-Системы проектирования", Россия Все права защищены

Инд. № подл.	Подп. и дата
Взам. инв. №	Инд. № дцкл.
Подп. и дата	Подп. и дата

Изм.	Лист	№ докум.	Подп.	Дата
------	------	----------	-------	------

МГТУ.24У536.СС